

Carlyle/Eisenhower East Design Review Board (DRB)

Keep this sheet for your records.

Filing Deadline: Dec. 19, 2023

DRB Public Hearing Date: Jan. 18, 2023

STAFF REPORTS

Staff reports outlining staff's recommendation to the Board for approval or deferral of each case will be emailed to applicants approximately five (5) days prior to the hearing date. Staff reports may also be available on the City's website at

<http://alexandriava.gov/planning/info/default.aspx?id=43130>. Call the Department of Planning and Zoning at (703) 746-4666 with questions.

AFTER THE HEARING

After final approval is granted, staff will email the updated staff report with the Design Review Board determination to the applicant. Most projects require building permits before construction can begin. Contact the Department of Code Administration at (703) 746-4200 to determine if a building permit is needed.

Carlyle/Eisenhower East Design Review Board (DRB) Application

PROJECT NAME: Hoffman CDD #2 BLOCKS: 2, 3, 7, 14, 9, 11, 12, 20

ADDRESS OF PROJECT: See attached "Property Description Attachment"

APPLICATION FOR REVIEW OF: *(Check one)*

- ☐ Building ☐ Concept ☐ Final
☐ Sign
☐ Awning
☒ Other: CDD Concept Plan

APPLICANT Name: Hoffman Companies & Paradigm Development Cos.

Address: 2461 Eisenhower Ave. Alexandria, VA & 1515 N. Courthouse Rd. Ste. 600, Arl. VA

Phone: Ken Wire 202-431-3624 (Hoffman) Email Address: kwire@wiregill.com
Mary Catherine Gibbs 703-835-1922 (Paradigm) mcgibbs@wiregill.com

ARCHITECT/DESIGNER Name: N/A

Address: _____

Phone: _____ Email Address: _____

PROPERTY OWNER Name: See attached "Property Description Attachment"
(if different from APPLICANT)


Address: _____

Phone: _____ Email Address: _____

DESCRIBE THE REQUEST BRIEFLY: CDD #2 Concept Plan

The undersigned hereby attests that all of the information herein provided including the site plan, building elevations, prospective drawings of the project, and written descriptive information are true, correct and accurate. The undersigned further understands that, should such information be found incorrect, any action taken by the Board based on such information may be invalidated. The applicant, if other than the property owner, also attests that he/she has obtained permission from the property owner to make this application.

Note: Per condition #67 of the Carlyle SUP #2253, as amended by SUP #2007-0094, all applicants will be responsible for the costs associated with DRB review of the application. Fees are determined based upon the number of applicants per hearing. Applicants will be notified by Planning and Zoning staff of the amount owed after the filing deadline has passed and the agenda for the hearing has been finalized. Payment is expected prior to the request being acted upon by the DRB.

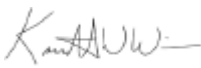Applicant Attorney Signature: 
Applicant Printed Name: Kenneth W. Wire

Date: 12/19/23

Property Description Attachment

Tax Map No.	Address	Owner	
072.02-02-12	2425 Mill Road	Hoffman Family LLC	Block 3A & 3B
072.03-04-09	312 Taylor Drive	Hoffman Management Inc.	Block 2A & 2B
072.04-04-08	315 Stovall St.	Hoffman Family LLC	Blocks 2A & 2B
072.04-03-38	206 Hoffman St.	Hoffman Family LLC	Block 7
072.04-03-26	2380 Mill Road	Town Center Garage LLC	Block 14
078.02-01-08	2400 Eisenhower Ave.	Hoffman Family LLC	Block 9A & 9B
075.02-01-13	2300 Dock Lane	Hoffman Towers Block 11 LLC	Block 11
078.02-01-09	2356 Eisenhower Ave.	Hoffman Towers Block 12 LLC	Block 12
Paradigm Properties	<i>*See Application under Separate cover*</i>		
078.02-01-22	2250 Dock Lane	Mill Road Block 20 LLC, c/o Paradigm Development Company, LLC	Block 20
078.02-01-23	2200 Dock Lane	Block 20 A LLC, c/o Paradigm Development Company, LLC	Block 20

Carlyle/Eisenhower East Design Review Board (DRB) Filing Instructions

Filing Deadlines

- Applications for DRB review must be submitted no later than thirty (30) calendar days prior to the scheduled DRB meeting.
- Contact the DRB staff at the number below at least a week prior to filing to coordinate submissions by the filing deadline. DRB staff will request that PDFs of draft submissions be emailed to P&Z for pre-review and comment. Staff will notify applicants of any suggested design/content revisions to submissions to be made by the filing deadline.
- A schedule of submission dates is maintained in the Department of Planning and Zoning and is also posted at: <http://alexandriava.gov/planning/info/default.aspx?id=43130>
- All applications are due by 5:00 p.m. on the day of the application filing deadline.
- If no applications are received by the submission deadline for a given hearing, that hearing will be cancelled.

Application Support Materials

- All supporting materials (see attached checklist) must be submitted by the **filing deadline** (see above). **New material may not be submitted or presented at the DRB hearing.**
- Applications without the required supporting materials are deemed incomplete and will not be heard by the DRB.

**For assistance with any of these procedures contact P&Z
Development Staff at (703) 746-4666.**

Carlyle/Eisenhower East Design Review Board (DRB)

Application Checklist for Buildings in CONCEPT REVIEW*:

N/A Physical massing model at minimum 1"=30', showing existing and proposed buildings for all adjacent properties

N/A **Submit the following plan copies containing all of the information on this checklist:**

N/A Twelve (12) 11"x17" collated, stapled color sets

N/A One (1) 24"x36" collated, stapled, color sets, and

X One (1) 11"x17" 120 dpi PDF file

X Number all sheets in plan set

Zoning tabulations (for each element, list zoning ordinance requirement and number proposed):

X Zoning of the site

X Existing uses on the site

X Proposed uses for the site

X Lot area(s) (and minimum lot area required under zoning, if applicable)

X Number of dwelling units (list by number of bedrooms for multifamily)

X Units per acre for residential

X Gross square feet (GSF) of building area, total and listed by use (with area devoted to parking included and listed separately)

N/A, unknown Net square feet (NSF) of floor area, total and listed by use

N/A, unknown Existing and proposed floor-area-ratios

X Open space total provided and broken down by ground-level space and usable space provided

N/A, unknown Average finish grade for each building

X Height of each building above average finish grade

X Building setbacks with required and proposed listed separately

N/A Frontage with required and proposed listed separately

N/A Parking spaces (listed by compact, standard, handicapped size and total)

N/A Loading spaces (number required and number proposed)

Site plan/architecture:

N/A Color Site plan at appropriate scale, showing approved uses & heights for adjacent properties

N/A Color Landscape concept plan showing hardscape and planting areas, trees, street furniture, etc.

N/A Color typical floor plans at min. 1/16" = 1'-0" for all levels including roof

N/A Building elevations in color at min. 1/16" = 1'-0" of all building faces with materials labeled, rendered with shadows and keyed to plans

N/A Building/site sections showing grade changes in relationship to buildings and/or retaining walls, rendered with shadows and keyed to plans and showing average finish grade line and heights, including penthouses

N/A Enlarged details (plan/section/elevation) of typical bays at pedestrian level as required

N/A Street-level perspective views in color

N/A Building solid/void area ratio calculation drawings and tabulations

Carlyle/Eisenhower East Design Review Board (DRB)

Application Checklist for Buildings in FINAL REVIEW*:

- _____ Detailed physical building model at appropriate scale
- _____ **Submit the following plan copies containing all of the information on this checklist:**
- _____ **Twelve (12) 11"x17" collated, stapled color sets**
- _____ **One (1) 24"x36" collated, stapled, color sets, and**
- _____ **One (1) 11"x17" 120 dpi PDF file**
- _____ **Number all sheets in plan set**

Zoning tabulations (for each element, list zoning ordinance requirement and number proposed):

- _____ Zoning of the site
- _____ Existing uses on the site
- _____ Proposed uses for the site
- _____ Lot area(s) (and minimum lot area required under zoning, if applicable)
- _____ Number of dwelling units (list by number of bedrooms for multifamily)
- _____ Units per acre for residential
- _____ Gross square feet (GSF) of building area, total and listed by use (with area devoted to parking included and listed separately)
- _____ Net square feet (NSF) of floor area, total and listed by use
- _____ Existing and proposed floor-area-ratios
- _____ Open space total provided and broken down by ground-level space and usable space provided
- _____ Average finish grade for each building
- _____ Height of each building above average finish grade
- _____ Building setbacks with required and proposed listed separately
- _____ Frontage with required and proposed listed separately
- _____ Parking spaces (listed by compact, standard, handicapped size and total)
- _____ Loading spaces (number required and number proposed)

Site plan/architecture:

- _____ Color Site plan at appropriate scale, showing approved uses & heights for adjacent properties
- _____ Color Landscape concept plan showing hardscape and planting areas, trees, street furniture, etc.
- _____ Color typical floor plans at min. 1/16" = 1'-0" for all levels including roof
- _____ Building elevations in color at min. 1/16" = 1'-0" of all building faces with materials labeled, rendered with shadows and keyed to plans
- _____ Building/site sections showing grade changes in relationship to buildings and/or retaining walls, rendered with shadows and keyed to plans and showing average finish grade line and heights, including penthouses
- _____ Street-level perspective views in color
- _____ Building solid/void area ratio calculation drawings and tabulations
- _____ Landscape details, referenced to Color Landscape plan
- _____ Enlarged details (plan/section/elevation) of all building setbacks with dimensions
- _____ Wall sections with enlarged details indicating different conditions at building setbacks
- _____ Additional materials requested by the DRB or materials required by conditions of approval (if applicable): List: _____

**Color and material boards and samples to be provided at Board hearing*

- _____ Additional materials requested by the DRB or materials required by conditions of approval (if applicable): List: _____

Carlyle/Eisenhower East Design Review Board (DRB)

Application Checklist for Signs, Awnings, Other:

_____ Submit twelve (12) 11"x17" (minimum size) collated, stapled color sets (w/pages numbered) and one (1) 11"x17" 120 dpi resolution PDF file of the following:

_____ Color Site plan at a measurable scale showing:

- location(s) of proposed element(s)
- dimensions of storefront and building widths [FOR SIGNS & AWNINGS ONLY]

_____ Large-scale elevations and sections with enlarged details

_____ Elevations in color at min. 1/16" = 1'-0", with materials labeled, rendered with shadows and keyed to plans

_____ Street-level perspective photomontages in color (daytime view)

_____ Street-level perspective photomontages in color (nighttime view) [FOR SIGNS ONLY]

_____ Additional materials requested by the DRB or materials required by conditions of approval (if applicable): List: _____

Design guidelines (provide information needed to assess compliance):

_____ If located within the Carlyle CDD, information required by the *Carlyle Design Guidelines* and the *Carlyle Streetscape Design Guidelines*


_____ If located in the Eisenhower East CDD, information required by the *Eisenhower East Design Guidelines*

GENERAL NOTES

1. THE CITY OF ALEXANDRIA TAX ASSESSMENT MAP NUMBERS FOR THIS SITE ARE 078.02-01-08, 078.02-01-09, 078.02-01-13, 078.02-01-22, 078.02-01-23, 072.02-02-12, 072.04-03-26, 072.04-03-38 072.03-04-08 AND 072.04-04-09.
2. THE SITE CONTAINS APPROXIMATELY 78.90 ACRES (ENTIRE CDD #2).
3. THE BOUNDARY SURVEY WAS PREPARED BY christopher consultants, Ltd. BETWEEN THE YEARS OF 1998 AND 2021.
4. THE TOPOGRAPHIC SURVEY WAS OBTAINED FROM christopher consultants, Ltd. BETWEEN THE DATES OF 1998 AND 2021.
5. THE SITE IS CURRENTLY DEVELOPED AS THE HOFFMAN TOWN CENTER. THERE ARE NO NATURAL FEATURES ON THE SITE THAT NEED TO BE PRESERVED OR PROTECTED. THERE IS A RESOURCE PROTECTION AREA (RPA) BUFFER ON SITE. MODIFICATIONS TO THIS AREA WILL BE IN ACCORDANCE WITH CURRENT CITY OF ALEXANDRIA REQUIREMENTS FOR REDEVELOPMENT WITHIN THE RPA. THERE IS A WETLAND OF MINIMAL ECOLOGICAL VALUE ON THE PROPERTY AND ANY PERMITS REQUIRED FROM THE COE WILL BE OBTAINED.
6. ADVERSE IMPACTS TO NEIGHBORING PROPERTIES FROM INTENSITY OF DEVELOPMENT RESULTING FROM A FUTURE DSUP WILL BE MITIGATED THROUGH GREEN BUILDING PRACTICES, TPMs, AFFORDABLE HOUSING, DEVELOPER CONTRIBUTIONS, NEW ROADWAYS AND STREETSCAPES, OPEN SPACE, DEVELOPMENT CONDITIONS, ETC. ALL SPECIFIED DURING THE DSUP PUBLIC REVIEW PROCESS.
7. REFER TO THE TABLE ON SHEET C200 FOR THE MAXIMUM HEIGHT OF ANY BUILDING ON THIS SITE.
8. THE PROJECT WILL MEET THE PARKING REQUIREMENTS AS PART OF THE DSUP PROCESS FOR EACH BLOCK. (5-604-C (8)).
9. SIGNIFICANT GROUND LEVEL PUBLIC OPEN SPACE TO BE CREATED AS PART OF THE PROJECT. SUSTAINABILITY GOALS, STORMWATER MANAGEMENT IMPROVEMENTS AND SPECIFIC AMENITIES FOR EACH BLOCK TO BE DETERMINED AT EACH DSUP SUBMISSION. (5-604-C (9); (5-604-C (11)). REFER TO THE CHART ON SHEET C200 FOR AMOUNT OF OPEN SPACE PROVIDED. AS PART OF THIS CDD, THERE WILL BE PEDESTRIAN AND BICYCLE NETWORK IMPROVEMENTS. THE DETAILS OF THE IMPROVEMENTS WILL BE PROVIDED AT THE TIME OF THE DSUP PROCESS FOR EACH BLOCK, BUT REFER TO SHEET C500 FOR A SCHEMATIC LAYOUT OF BICYCLE NETWORK IMPROVEMENTS.
10. TO THE BEST OF OUR KNOWLEDGE THERE ARE NO MARINE CLAYS ON SITE. (5-604-C (14)).
11. TO THE BEST OF OUR KNOWLEDGE CONTAMINATED SOIL MAY BE ON SITE. (5-604-C (15)).
12. FOR BLOCKS 2, 3 AND 9 THERE MAY BE UNUSUAL AND SPECIFIC SITUATIONS, SUCH AS BLOCK SHAPE, SIZE, AND GEOMETRY, WHERE THE APPLICANT CAN DEMONSTRATE IT IS INFEASIBLE TO PROVIDE ACTIVE SCREENING OR ARCHITECTURAL TREATMENTS THAT ARE INDISTINGUISHABLE FROM ACTIVE SCREENING AS RECOMMENDED BY THE PLAN. IN THOSE CASES THE APPLICANT WILL DEMONSTRATE HOW THE PROJECT MEETS THE SAP URBAN DESIGN GOALS.

COORDINATED DEVELOPMENT DISTRICT #2 CONCEPTUAL DESIGN PLAN ALEXANDRIA, VIRGINIA

VICINITY MAP
SCALE 1"= 350'

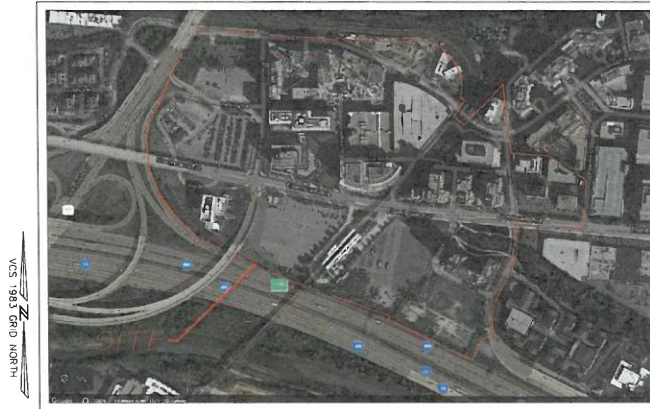

PROJECT NARRATIVE

THE APPLICANTS ARE FILING THIS CDD CONCEPT PLAN FOR CDD #2 TO ADDRESS BLOCKS 2, 3, 7, 9, 11, 12, 14 AND 20. THIS AREA INCLUDED AS PART OF CDD SHALL STILL COMPLY WITH THE GUIDELINES SET FORTH IN THE EISENHOWER EAST SMALL AREA PLAN (EESAP). THE APPLICANT SEEKS AN OPTION TO REMOVE BLOCK 3 ROAD, OPEN SPACE, BIKE CONNECTIONS, AND COMPLETE STREETS WILL BE PROVIDED IN THIS CDD PER THE EESAP GUIDELINES TO PROMOTE GROWTH AND CONNECTIVITY BETWEEN THE BLOCKS WITHIN THE EISENHOWER EAST AREA.

ALL OTHER BLOCKS WITHIN THIS CDD THAT ARE NOT PART OF THIS APPLICATION AND ARE INCLUDED FOR REFERENCE ONLY.

SHEET INDEX	
C000	COVER SHEET
C100	EXISTING CONDITIONS PLAN
C200	PROPERTY OWNERSHIP INFORMATION
C300	CDD CONCEPT PLAN
C301	BLOCK 3 ALTERNATE LAYOUT EXHIBIT
C400	OPEN SPACE EXHIBIT
C500	BIKE CONNECTION EXHIBIT
C600	STREET CROSS SECTION EXHIBIT
C700	STREET HIERARCHY
C701	SOUTHERN STREET UNDER WMATA TRACKS EXHIBIT

PROFESSIONAL SEAL AND SIGNATURE	DATE	REVISION
	06-11-2022	FIRST SUBMISSION
	07-26-2022	SECOND SUBMISSION
	09-25-2023	THIRD SUBMISSION
	11-05-2023	FOURTH SUBMISSION

APPLICANT

HOFFMAN FAMILY, LLC
2034 EISENHOWER AVE, SUITE 290
ALEXANDRIA, VA 22331

APPLICANT

PARADIGM DEVELOPMENT
COMPANY, LLC
1515 NORTH COURTHOUSE ROAD, SUITE 600
ARLINGTON, VA 22201

CIVIL ENGINEER

CHRISTOPHER CONSULTANTS, LTD.
4035 RIDGE TOP ROAD
SUITE 601
FAIRFAX, VIRGINIA 22030

ATTORNEY


WIRE GILL
700 N FAIRFAX ST
SUITE 600
ALEXANDRIA, VA 22314
(NEN WIRE REPRESENTING HOFFMAN FAMILY, LLC)
(MARY CATHY RINE CROSS REPRESENTING PARADIGM DEVELOPMENT COS)

ARCHITECT


COOPER CARRY
625 N WASHINGTON ST., STE. 200,
ALEXANDRIA, VA 22314

Block	Principle Land Use	Minimum Percentage Commercial	Minimum Building Height (ft.)	Minimum Building Height (ft.)	Required On-Site Accessible Open Space (sq. ft.)	Approximate Block Area (Ac.)	Approximate Block Area (sq. ft.)	Project Total GSF Without GSF Storage (sf)	Retail Focus Areas	Proposed For Redevelopment
Block 1	Residential and Commercial	N/A	150'	N/A	18,500	2.79	121,532	101,000	No	No
Block 2A/B	Residential and Commercial	30%	300'	150'	41,500	4.2	184,694	1,500,000	No	Yes
Block 3A/B	Residential and Commercial	30%	150'	125'	0	3.0	129,809	1,250,000	No	Yes
Block 4/5	Residential and Commercial	30%	150'	125'	10,800	5.1	220,849	1,755,000	Yes	No
Block 6A	Residential	0%	300'	150'	0	1.5	64,033	665,512	Yes	No
Block 6B/C	Residential and Commercial	60%	300'	150'	16,000	3.1	136,712	162,964	Yes	No
Block 7	Commercial	100%	300'	150'	0	2.3	91,040	79,000	Yes	No
Block 8	Commercial	100%	300'	175'	0	1.8	77,517	697,471	Yes	No
Block 9A	Residential and Commercial	100%	200'	150'	1.5	1.5	64,647	0	No	Yes
Block 9B	Residential and Commercial	60%	400'	200'	24,000	1.9	78,408	1,600,000	Yes	Yes
Block 10A	U/I/Open Space	0%	50'	N/A	0	3.1	133,424	8,000	No	Yes
Block 10B	U/I/Open Space	0%	50'	N/A	64,000	0.2	10,716	0	No	No
Block 11	Residential and Commercial	0%	400'	200'	40,000	2.4	104,544	1,300,000	No	Yes
Block 12	Residential and Commercial	0%	350'	175'	0	1.3	56,182	1,250,000	No	Yes
Block 13	Residential	0%	300'	150'	0	1.3	57,134	490,000	No	No
Block 14	Commercial	100%	250'	125'	0	2.8	120,661	18,000	No	No
Block 15/15A	Residential and Commercial	30%	200'	100'	0	2.3	100,188	490,772	No	No
Block 16	Commercial	100%	150'	75'	0	0.8	33,062	127,000	No	No
Block 17	Commercial	100%	250'	125'	0	1.3	54,450	450,000	No	No
Block 18	Residential	0%	300'	150'	0	1.5	63,598	525,000	No	No
Block 19	Residential	0%	300'	150'	15,000	2.3	101,495	432,000	No	No
Block 20	Residential and/or Commercial	0%	300'	150'	15,300	1.6	182,477	365,000	No	Yes
Block 21	Residential and/or Commercial	0%	250'	125'	0	1.2	53,578	402,000	No	No

- Notes:
1. Minimum percentage commercial area can be allocated between blocks to achieve minimum commercial area above.
 2. Open space can be transferred among blocks.
 3. Blocks highlighted in gray are included in the CDD Conceptual Design Plan.
 4. All properties above are located in CDD #2 zone.

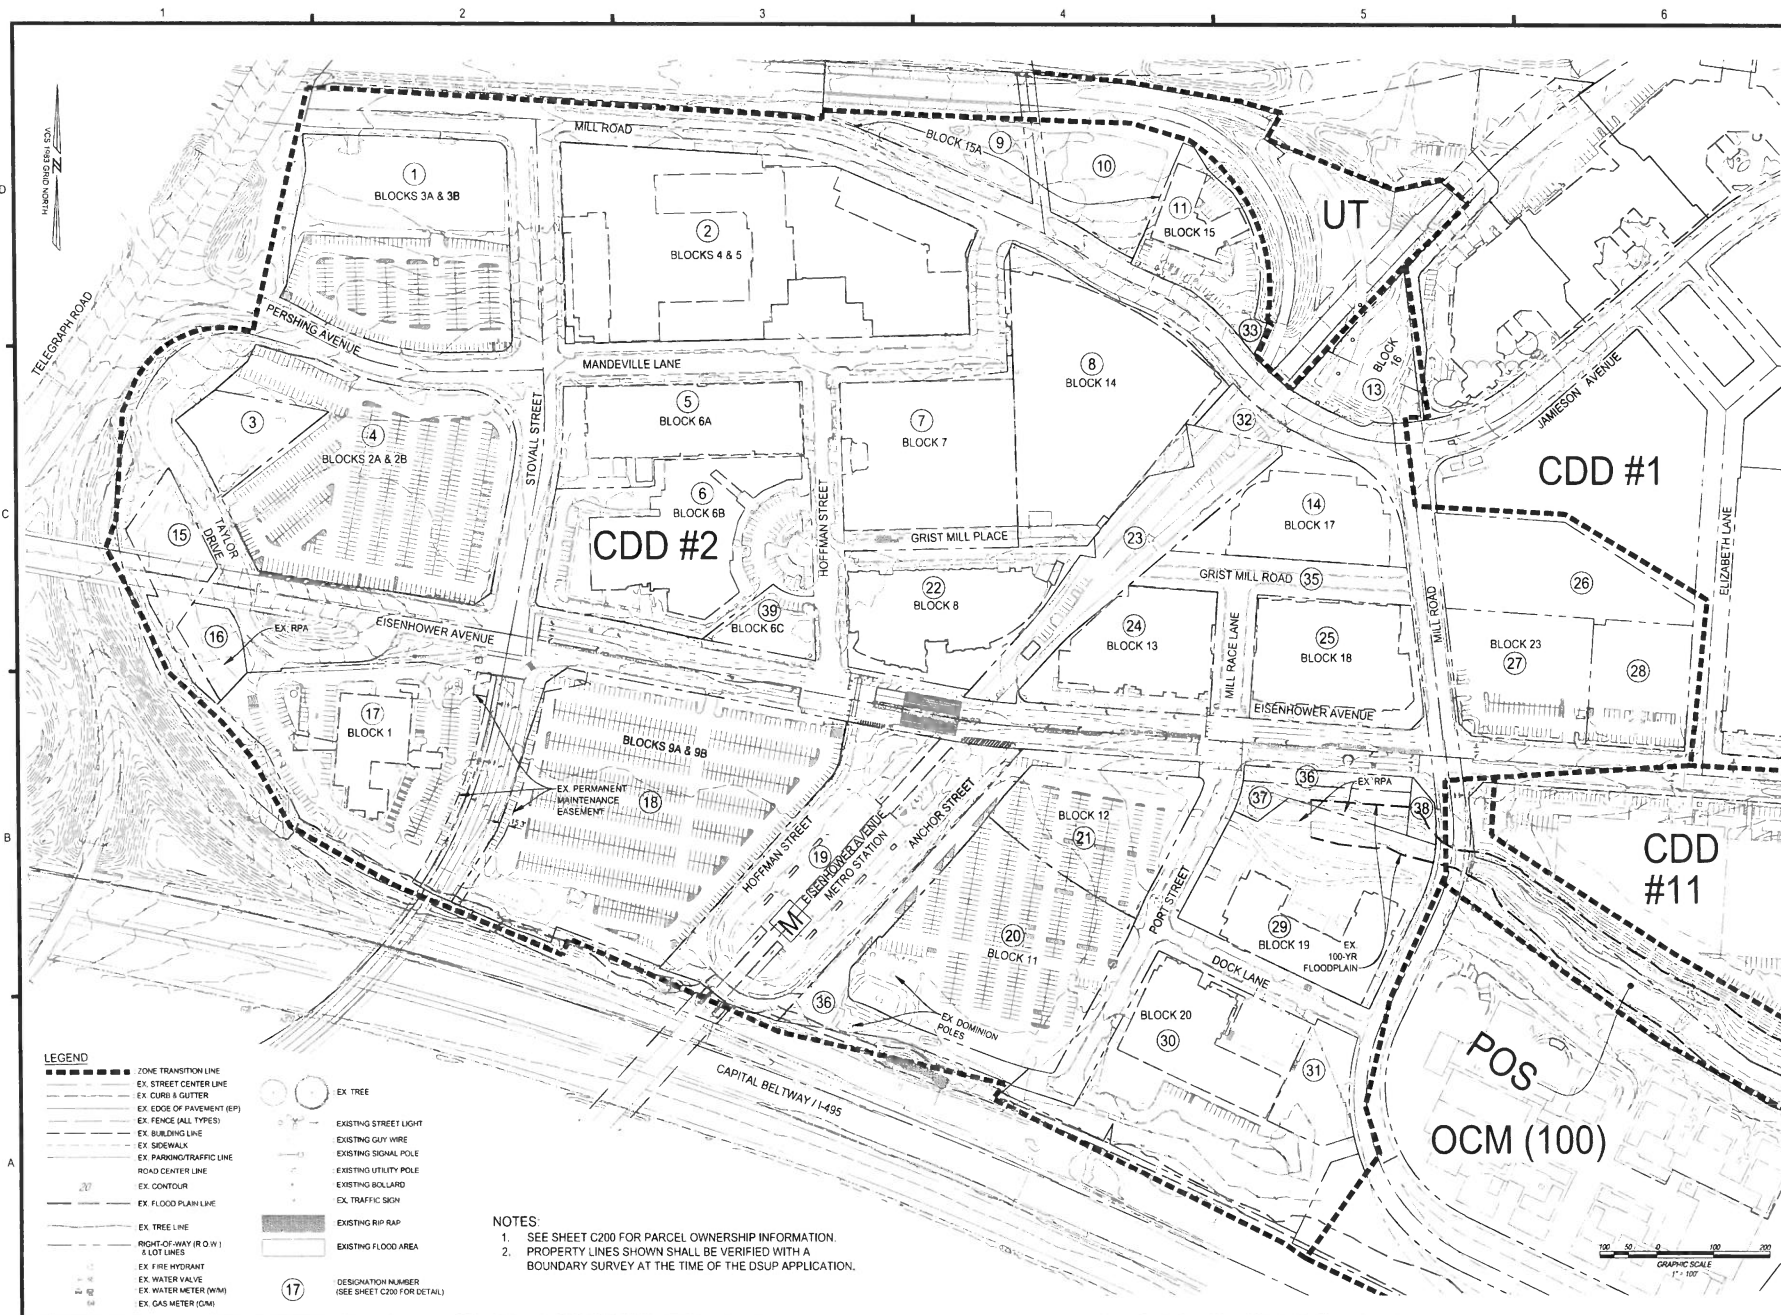

christopher consultants
4035 ridge top rd
suite 601
fairfax, va 22030
p 703.273.8620
engineering • surveying • land planning

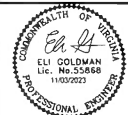

**COORDINATED DEVELOPMENT
DISTRICT #2
CONCEPTUAL DESIGN PLAN
CITY OF ALEXANDRIA, VIRGINIA**


NO.	DATE	DESCRIPTION
1	08-11-2022	CDD AMENDMENT SUBMISSION #1
2	07-11-2022	CDD AMENDMENT SUBMISSION #2
3	06-26-2023	CDD AMENDMENT SUBMISSION #3
4	11-03-2023	CDD AMENDMENT SUBMISSION #4
5		
6		
PROJECT No. 20005.003.00
DRAWING No. 111404
DATE: 02/11/22
SCALE: SEE SHEET
DESIGN: EG
DRAWN: MO
CHECKED: JMW

EXISTING CONDITIONS PLAN
SHEET No. **C100**

DESIGNATION	BLOCK	MAP #	ADDRESS	OWNER	USES	PROPOSED FOR REDEVELOPMENT
1	Blocks 3A & 3B	072.02-02-12	2425 Mill Rd.	Hoffman Family LLC	Vacant Land Commerc. (941)	YES
2	Blocks 4 & 5	072.04-03-41	2424 Mill Rd.	HTC 4/5 Project Owner LLC	General Commercial (400)	NO
3	Blocks 2A & 2B	072.03-04-09	312 Taylor Dr.	Hoffman Management Inc.	Vacant Land Commerc. (941)	YES
4	Blocks 2A & 2B	072.04-04-08	315 Stoval Sr.	Hoffman Family LLC	Vacant Land Commerc. (941)	YES
5	Block 6A	072.04-03-35	2472 Mandeville La.	Foundry Associates Owner LLC	Hi-Rise (7 ST and Up (330))	NO
6	Block 6B	072.04-03-34	2461 Eisenhower Av.	2461 Eisenhower Acquisitions LLC	Office Buildings (487)	NO
7	Block 7	072.04-03-38	206 Hoffman St.	Hoffman Family LLC	General Commercial (400)	NO
8	Block 14	072.04-03-26	2380 Mill Rd.	Town Center Garage LLC	Parking Garage (449)	NO
9	Block 15A	072.02-02-22	2425 Mill Rd.	Washington Metropolitan Area Transit Authority	Currently Not Available	NO
10	Block 15A	072.02-02-21	2401 Mill Rd.	Washington Metropolitan Area Transit Authority	Currently Not Available	NO
11	Block 15	072.02-02-10	2355 Mill Rd.	City of Alexandria	City Govt Bldgs (730)	NO
12	-	072.02-02-20	2395 Mill Rd.	Currently Not Available	Currently Not Available	NO
13	Block 16	072.04-02-19	2345 Mill Rd.	MFH Alexandria V LLC	Extended Stay (472)	NO
14	Block 17	072.04-0A-00	2318 Mill Rd.	Carlyle Overlook Condominium	Currently Not Available	NO
-	-	072.04-0A-ASCO-A	2318 Mill Rd.	American Society of Clinical Oncology Inc.	Currently Not Available	NO
-	-	072.04-0A-ASCO-B	2318 Mill Rd.	American Society of Clinical Oncology Inc.	Currently Not Available	NO
-	-	072.04-0A-RETAIL	2318 Mill Rd.	Carlyle Overlook Owner LLC	Currently Not Available	NO
-	-	072.04-0A-RP-MRP	2318 Mill Rd.	Carlyle Overlook Owner LLC	Currently Not Available	NO
15	-	072.03-04-11	310 Telegraph Rd.	Alexandria VA hotel Partners LLC	Vacant Land Commerc. (941)	NO
16	-	072.03-04-10	2468 Eisenhower Av.	Alexandria VA hotel Partners LLC	Vacant Land Commerc. (941)	NO
17	Block 1	072.04-04-07	2460 Eisenhower Av.	Alexandria VA hotel Partners LLC	Hotel and Motel (470)	NO
18	Blocks 9A & 9B	078.02-01-08	2400 Eisenhower Av.	Hoffman Family LLC	Vacant Land Commerc. (941)	YES
19	BLOCK 10A	078.02-01-02	2390 Eisenhower Av.	Washington Metropolitan Area Transit Authority	Wash Metro Tran Auth (750)	YES
20	BLOCK 11	078.02-01-13	2300 Dock La.	Hoffman Towers Block 11 LLC	Vacant Land - APT (930)	YES
21	Block 12	078.02-01-09	2356 Eisenhower Av.	Hoffman Towers Block 12 LLC	Vacant Land - APT (930)	YES
22	Block 8	072.04-03-32	2415 Eisenhower Av.	USGBF NSF LLC	Office Buildings (487)	NO
23	-	072.04-03-12	2391 Eisenhower Av.	Washington Metropolitan Area Transit Authority	Wash Metro Tran Auth (750)	NO
24	Block 13	072.04-03-23	2351 Eisenhower Av.	Eisenhower Residential LP	Hi-Rise (7 ST and Up (330))	NO
25	Block 18	072.04-03-21	2251 Eisenhower Av.	Carlyle Place Associates LLC	Hi-Rise (7 ST and Up (330))	NO
26	Block 23	073.03-01-07	2331 Mill Rd.	Eisenhower Mill Properties LLC	Currently Not Available	NO
27	Block 23	073.03-01-09	2121 Eisenhower Av.	Simpson Development Co.	Office Buildings (487)	NO
28	Block 23	073.03-01-08	2111 Eisenhower Av.	211 Eisenhower Avenue Limited Partnership	Office Buildings (487)	NO
29	Block 19	078.02-01-21	750 Port St.	Paradigm 2250 Mill LLC	Hi-Rise (7 ST and Up (330))	NO
30	Block 20	078.02-01-22	2250 Dock La.	Mill Road Block 20 LLC, C/O Paradigm Development Company, LLC	Hi-Rise (7 ST and Up (330))	YES
31	Block 20	078.02-01-23	2200 Dock La.	Block 20 A LLC, C/O Paradigm Development Company, LLC	Hi-Rise (7 ST and Up (330))	YES
32	-	072.04-03-08	2360 Mill Rd.	Washington Metropolitan Area Transit Authority	Wash Metro Tran Auth (750)	NO
33	BLOCK 15B	072.04-02-14	2375 Mill Rd.	City of Alexandria	City Govt Bldgs (730)	NO
34	-	072.04-02-20	2365 Mill Rd.	Washington Metropolitan Area Transit Authority	Wash Metro Tran Auth (750)	NO
35	-	072.04-03-22	2316 Mill Rd.	Mill Race Property Owners Association	Vacant Land Com Area (980)	NO
36	BLOCK 19	078.02-01-19	2310 Eisenhower Av.	Hoffman Family LLC	Vacant Land - APT (930)	NO
37	BLOCK 19	078.02-01-15	2250 Eisenhower Av.	Hoffman Family LLC	Vacant Land - APT (930)	NO
38	BLOCK 19	078.02-01-07	2290 Mill Rd.	City of Alexandria	City Pks/Playgrounds (731)	NO
39	Block 6C	072.04-03-33	2425 Eisenhower Av.	2425 Eisenhower Acquisitions LLC	Vacant Land Commerc. (941)	NO

1. ALL PROPERTIES LISTED ABOVE ARE LOCATED IN THE CDD #2 ZONE.
2. BLOCKS HIGHLIGHTED IN GRAY ARE INCLUDED IN THIS CDD CONCEPTUAL DESIGN PLAN.

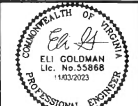


COORDINATED DEVELOPMENT
DISTRICT #2
CONCEPTUAL DESIGN PLAN
CITY OF ALEXANDRIA, VIRGINIA

[illegible]

PROJECT No.: 98085.065.00
DRAWING No.: 111404
DATE: 02.11.22
SCALE: N/A
DESIGN: EG
DRAWN: MQ
CHECKED: KMW

PROPERTY OWNERSHIP INFORMATION

SHEET No. C200

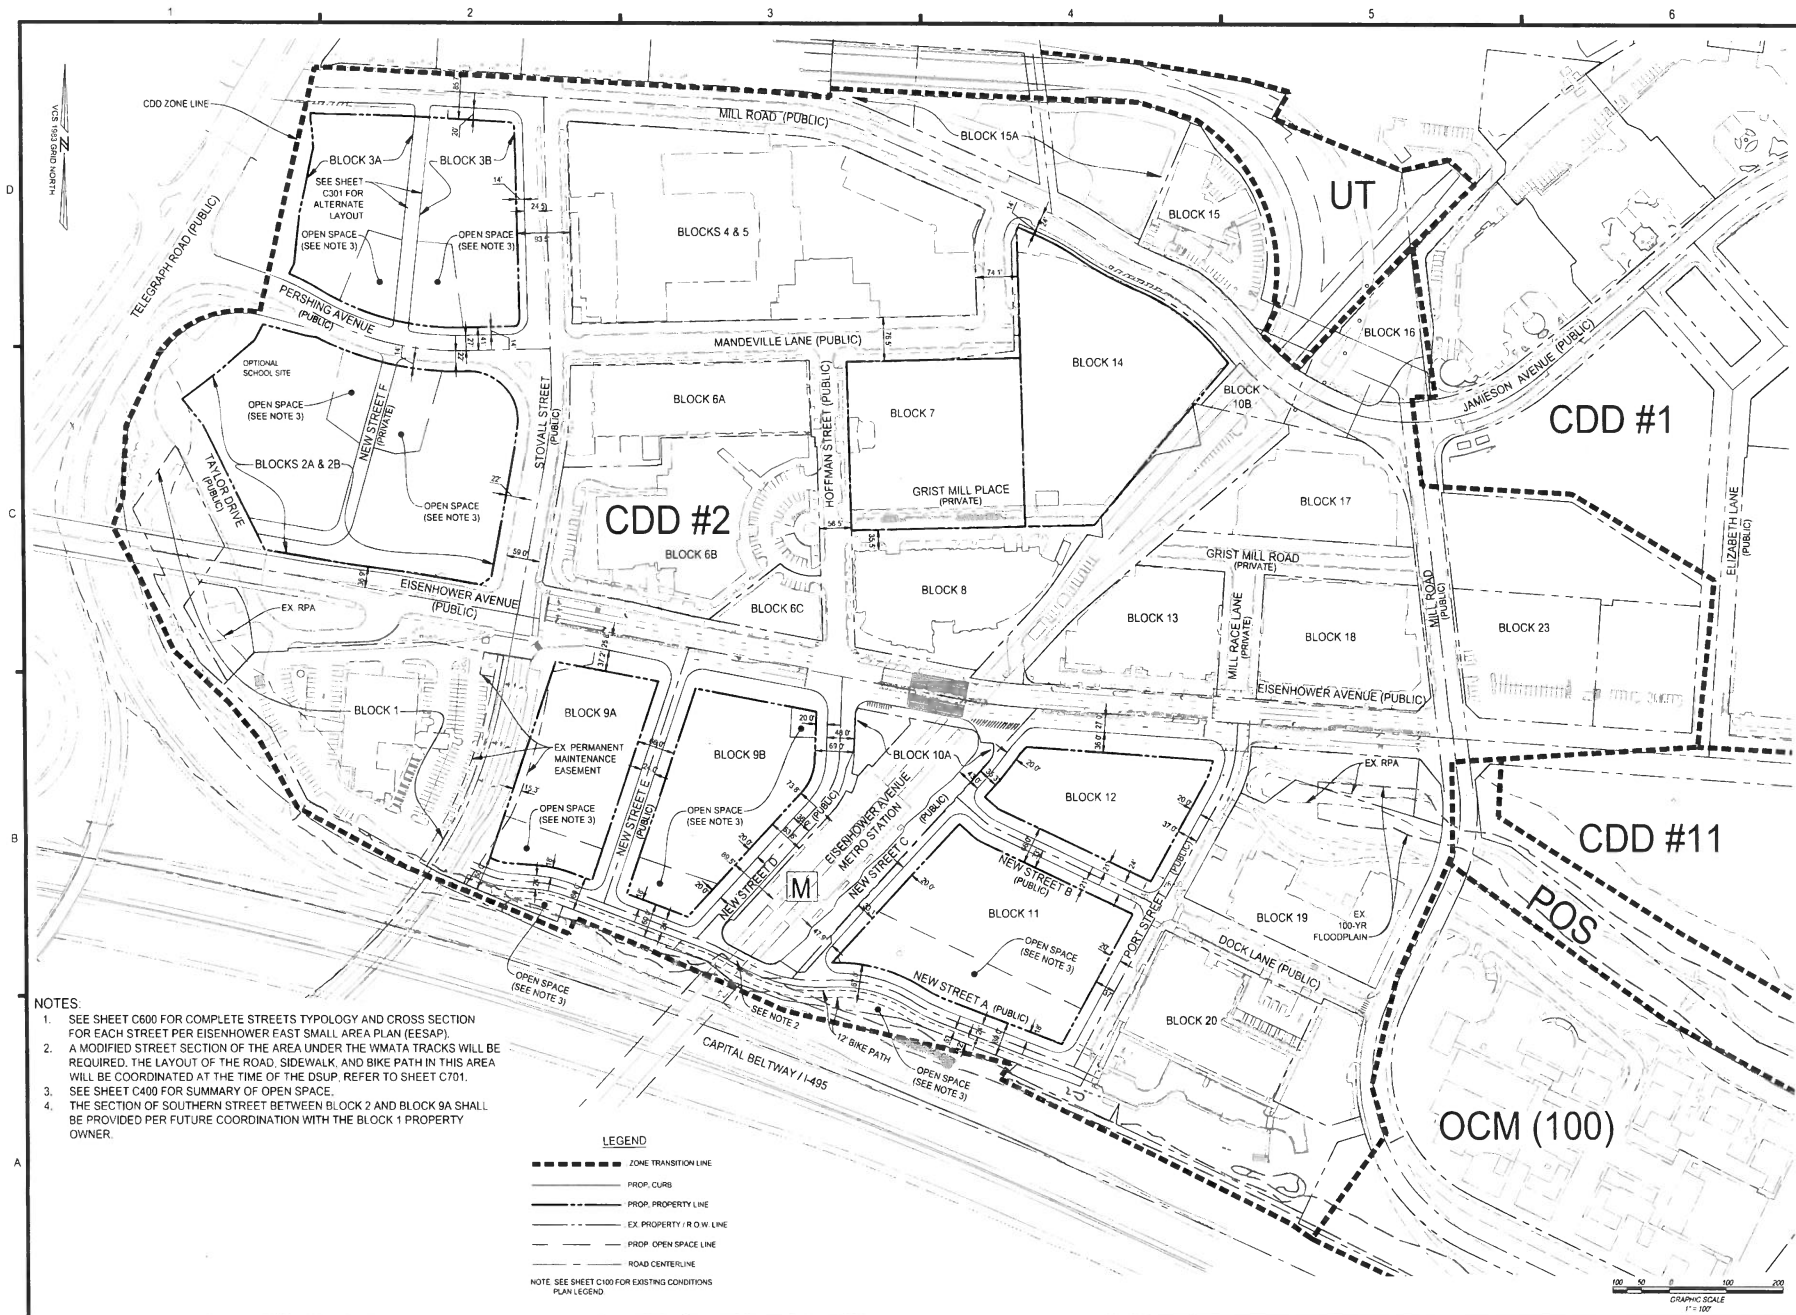

christopher consultants
4035 edge top rd
alexandria, va 22304
p 703.271.8820
engineering • surveying • land planning

ELI GOLDMAN
Lic. No. 55868
11/03/2023
PROFESSIONAL ENGINEER

COORDINATED DEVELOPMENT
DISTRICT #2
CONCEPTUAL DESIGN PLAN
CITY OF ALEXANDRIA, VIRGINIA

NO.	DATE	DESCRIPTION
1	02/11/2022	CDD AMENDMENT SUBMISSION #1
2	07/17/2022	CDD AMENDMENT SUBMISSION #2
3	08-26-2023	CDD AMENDMENT SUBMISSION #3
4	11-03-2023	CDD AMENDMENT SUBMISSION #4


PROJECT No. 98085.065.00
DRAWING No. 111404
DATE 02/11/22
SCALE SEE SHEET
DESIGN: ED
DRAWN: MD
CHECKED: MMW

SHEET TITLE


CDD CONCEPT PLAN

SHEET No.

C300

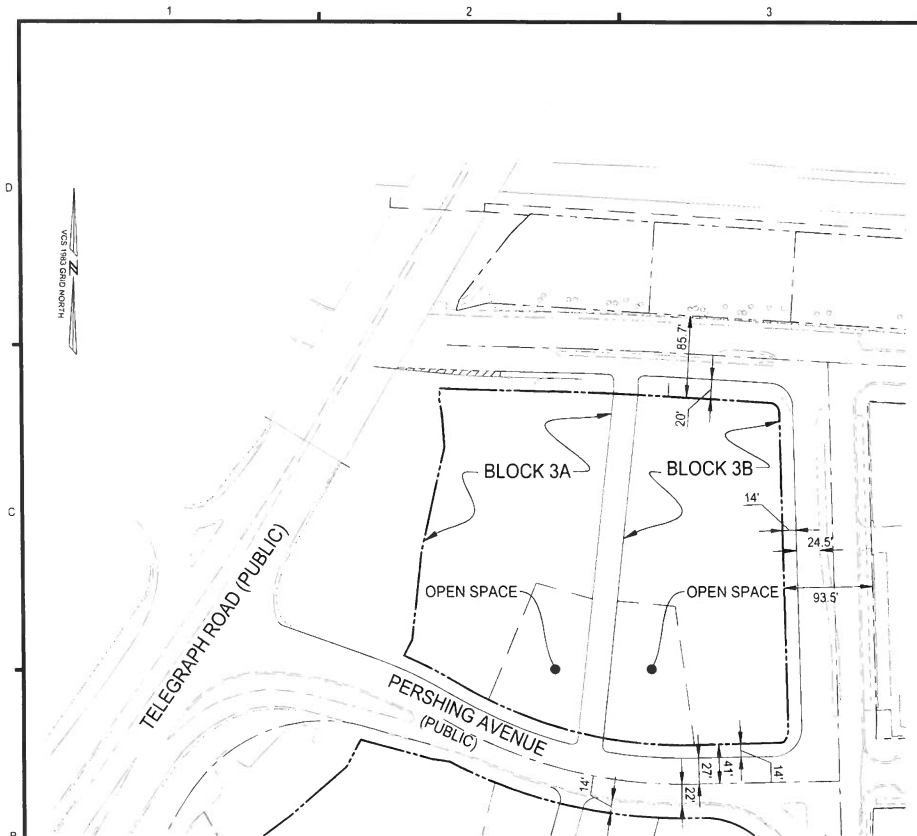

BLOCK 3 LAYOUT - WITH ROAD

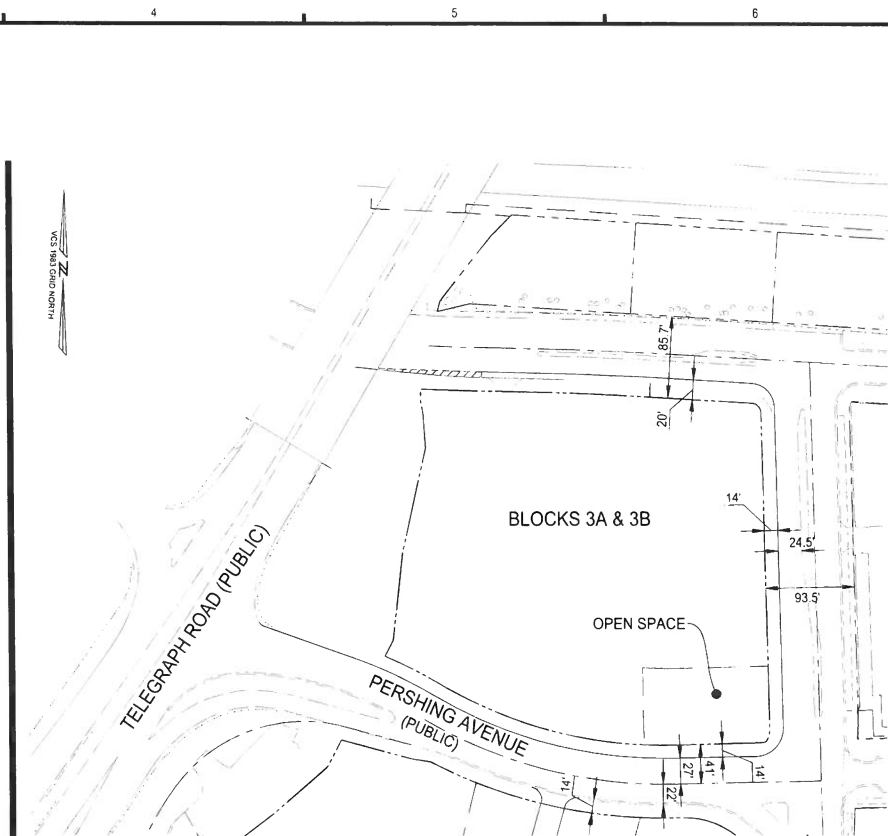

BLOCK 3 LAYOUT - WITHOUT ROAD

NOTE: INTERNAL ROAD NOT REQUIRED PROVIDED THAT PROPOSED DEVELOPMENT PROVIDES 45,000 SF OF GROUND FLOOR OR MULTI-FLOOR NON-RESIDENTIAL USE AND 10,000 SF OF AT-GRADE OPEN SPACE.

LEGEND

- ZONE TRANSITION LINE
- PROP. CURB
- PROP. PROPERTY LINE
- EX. PROPERTY / R.O.W. LINE
- PROP. OPEN SPACE LINE
- ROAD CENTERLINE

NOTE: SEE SHEET C100 FOR EXISTING CONDITIONS PLAN LEGEND.

christopher consultants
 4035 Ridge Top Rd
 Fairfax, VA 22033
 p 703.273.6820
 engineering • surveying • land planning




COORDINATED DEVELOPMENT
 DISTRICT #2
 CONCEPTUAL DESIGN PLAN
 CITY OF ALEXANDRIA, VIRGINIA


NO.	DATE	DESCRIPTION
1	02-11-2022	CDD AMENDMENT SUBMISSION #1
2	07-01-2022	CDD AMENDMENT SUBMISSION #2
3	08-26-2022	CDD AMENDMENT SUBMISSION #3
4	11-03-2023	CDD AMENDMENT SUBMISSION #4

PROJECT No.: 98085-Hoffman
 DRAWING No.: 111404
 DATE: 02-11-22
 SCALE: SEE SHEET
 DESIGN: EG
 DRAWN: MO
 CHECKED: MMW


SHEET TITLE:
**BLOCK 3
 ALTERNATE
 LAYOUT**

SHEET No.
C301

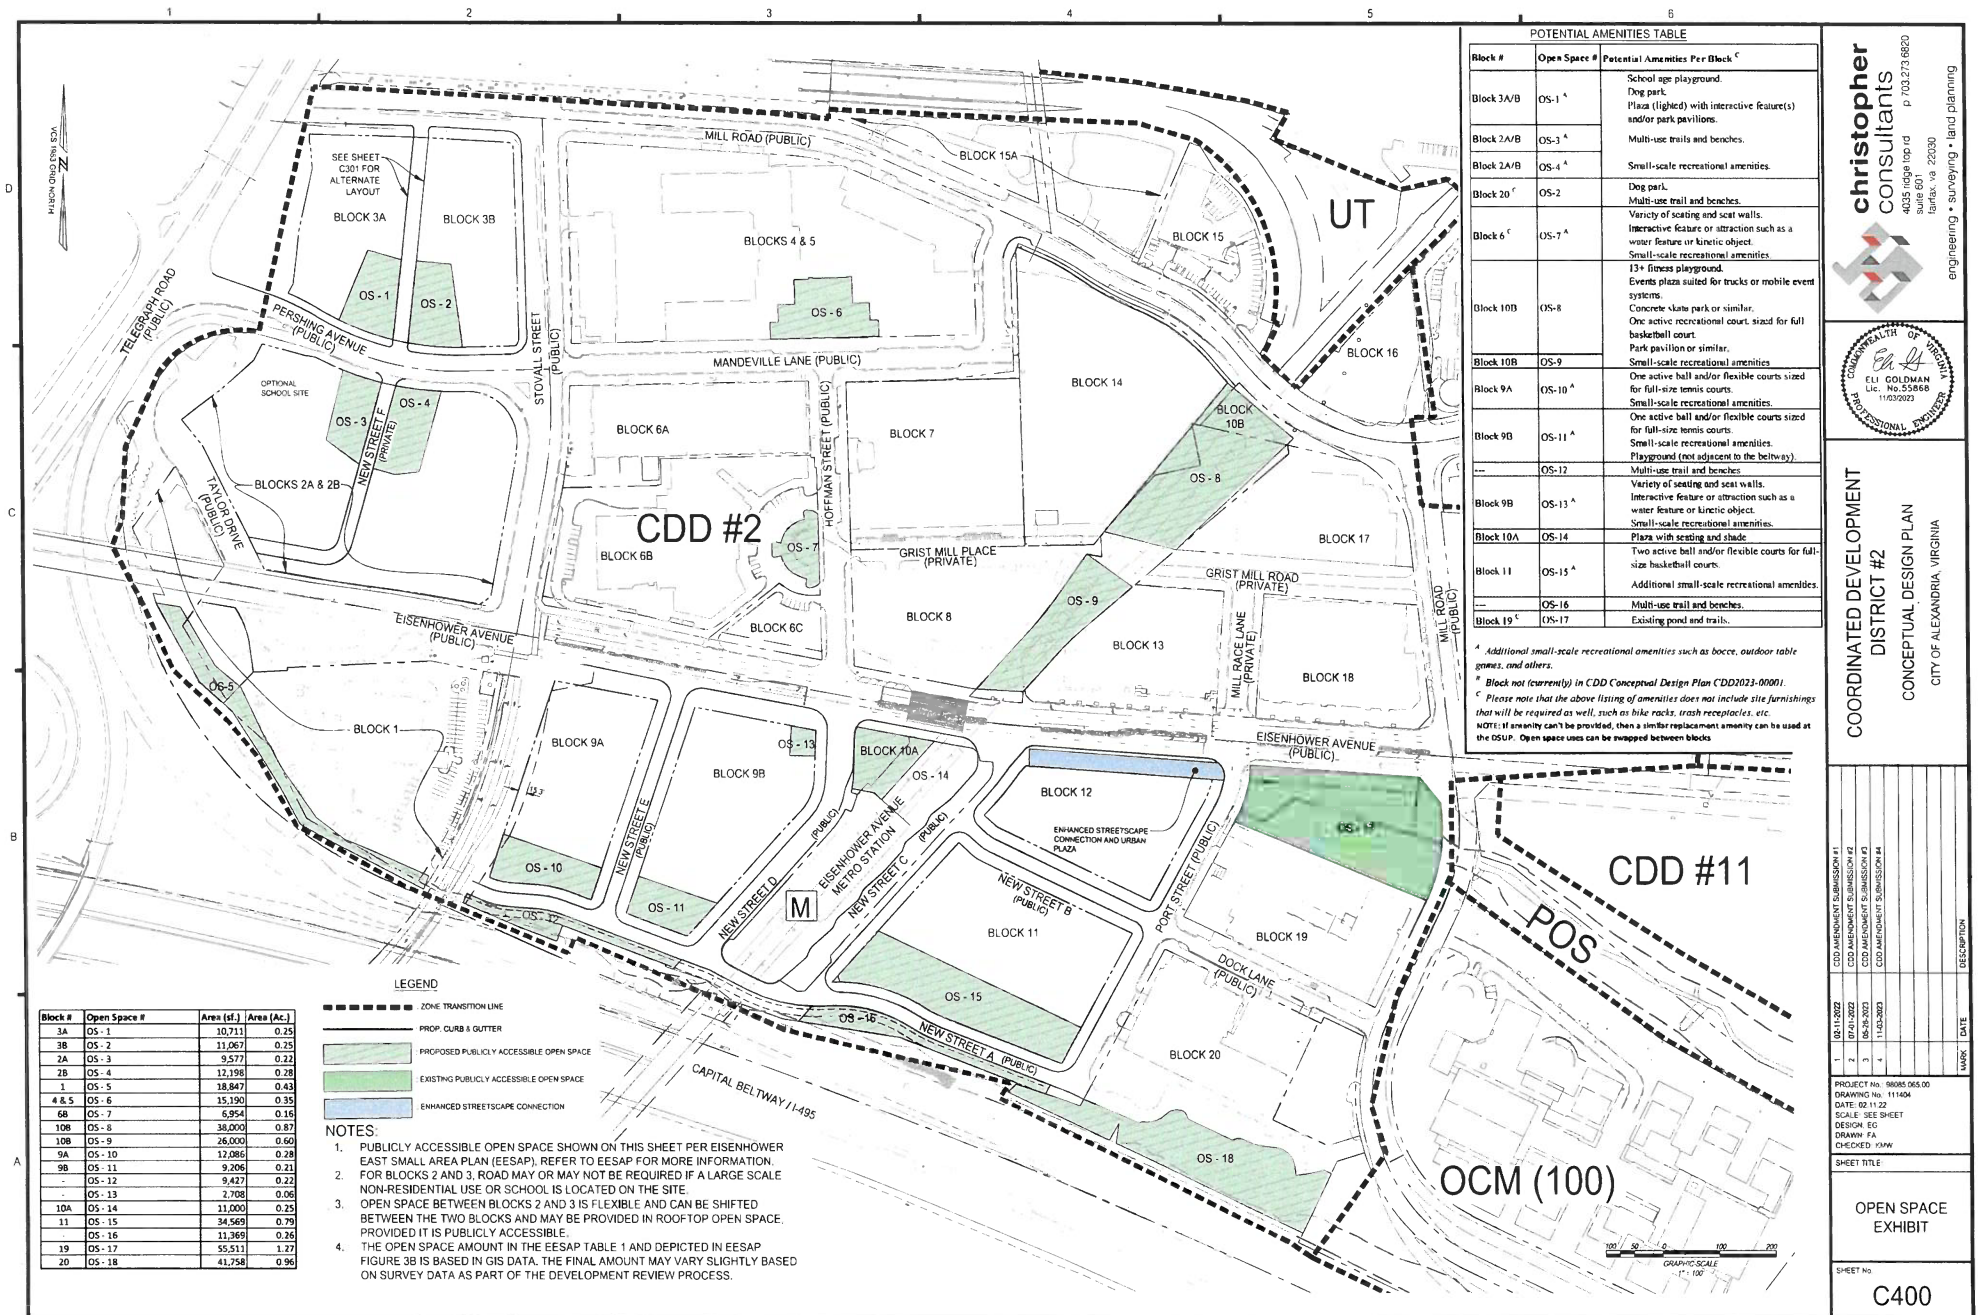

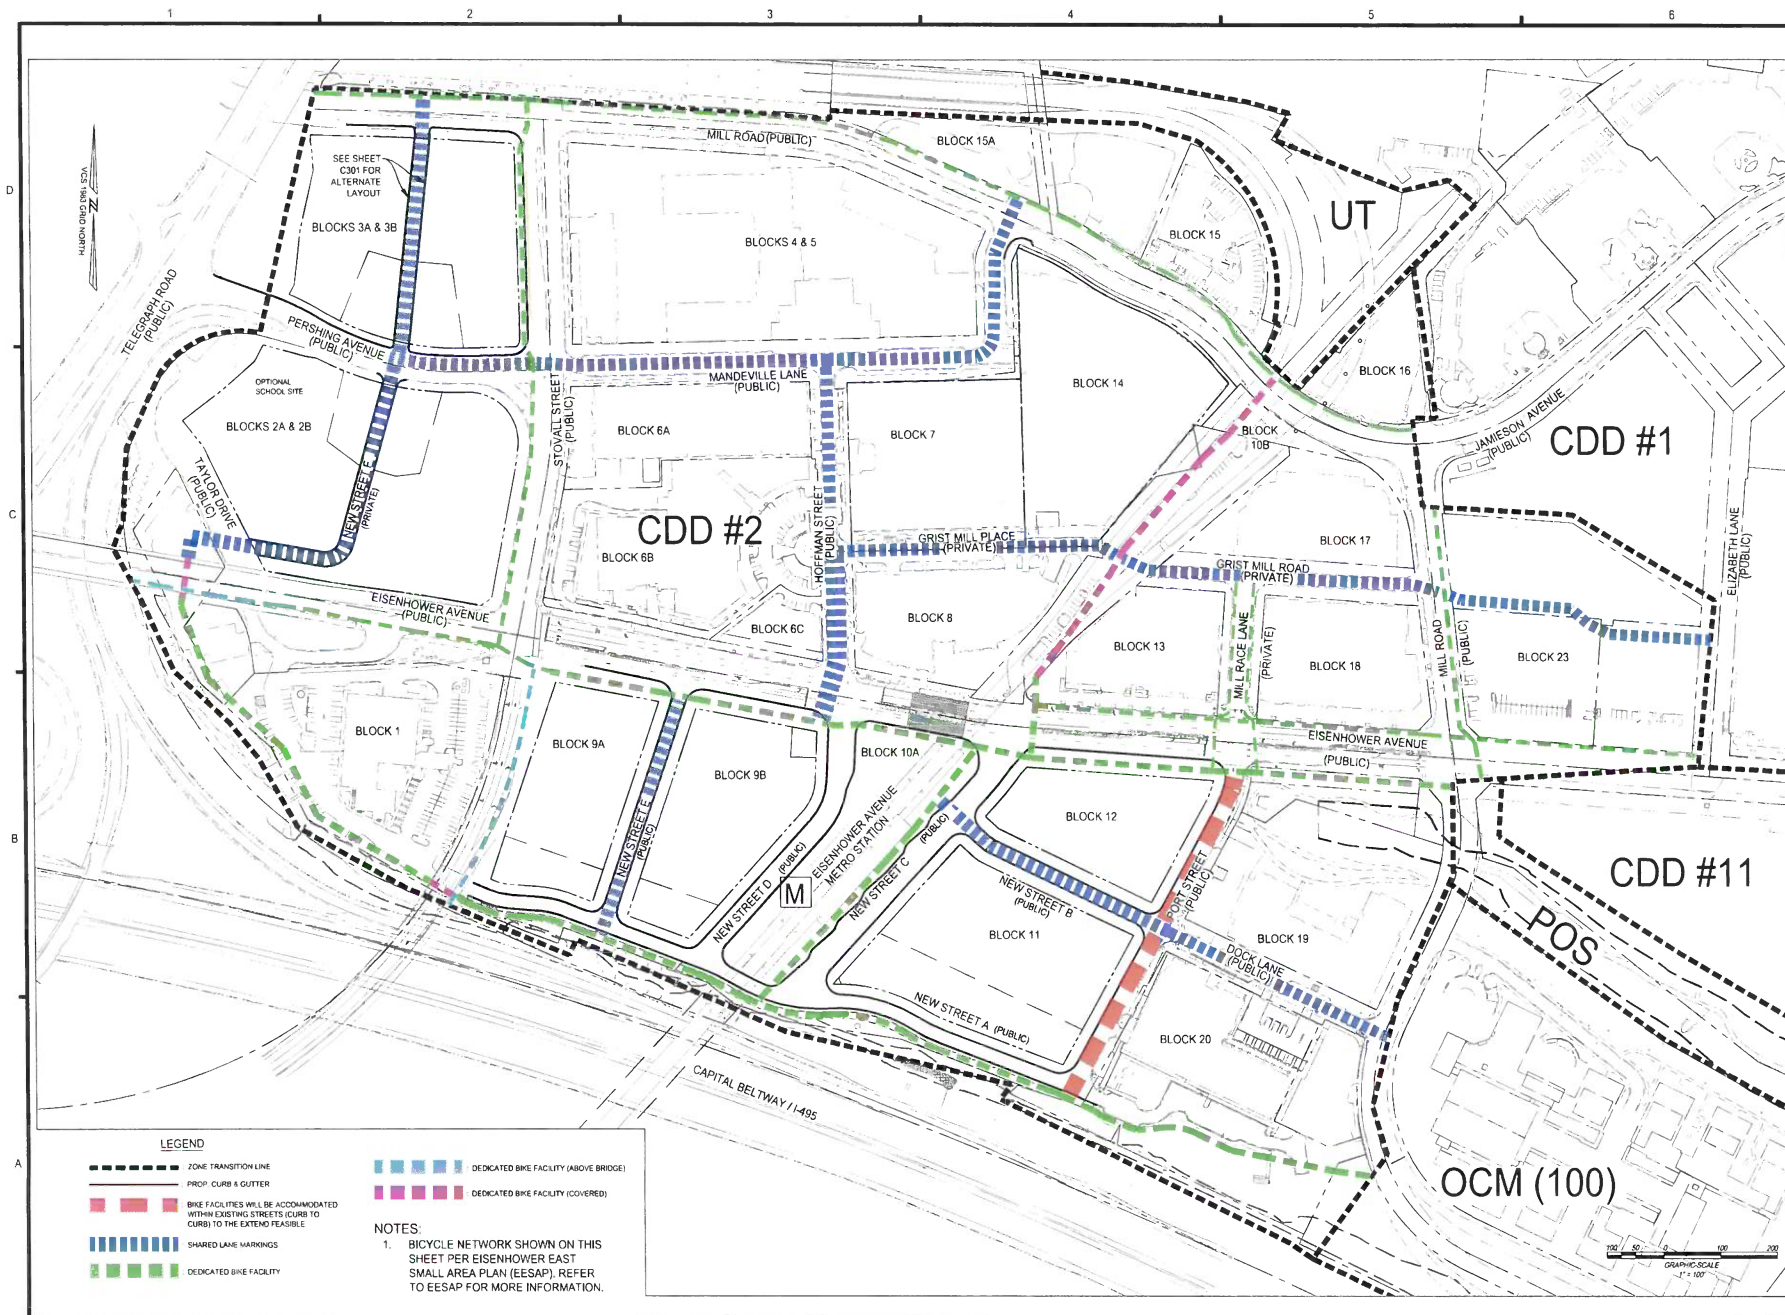

christopher consultants
 4035 edge top rd
 Fairfax, VA 22030
 p 703.273.8820
 engineering • surveying • land planning

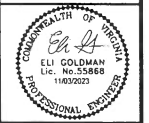









COORDINATED DEVELOPMENT DISTRICT #2
CONCEPTUAL DESIGN PLAN
 CITY OF ALEXANDRIA, VIRGINIA

NO.	DATE	DESCRIPTION
1	08/11/2022	CDD AMENDMENT SUBMISSION #1
2	07/27/2022	CDD AMENDMENT SUBMISSION #2
3	06/25/2022	CDD AMENDMENT SUBMISSION #3
4	11/02/2022	CDD AMENDMENT SUBMISSION #4

PROJECT No: 98085.065.00
 DRAWING No: 111404
 DATE: 02/11/22
 SCALE: SEE SHEET
 DESIGN: EG
 DRAWN: FA
 CHECKED: KMW

BIKE CONNECTION EXHIBIT

SHEET No: **C500**

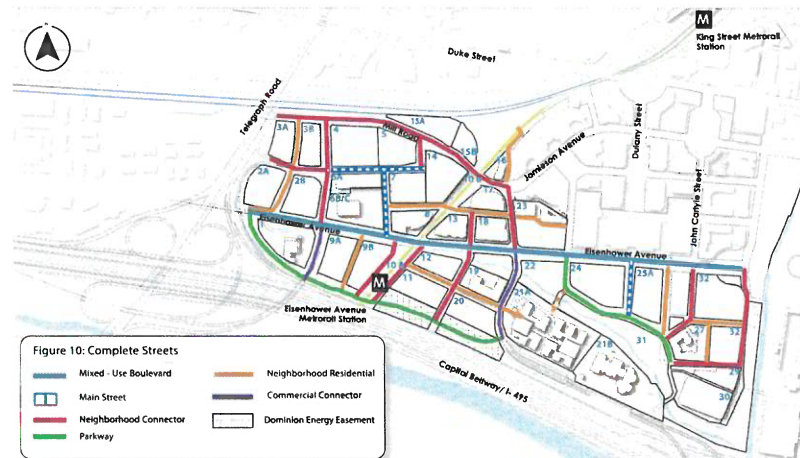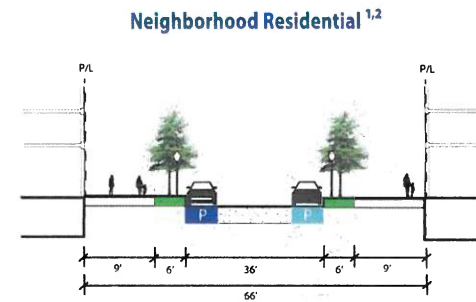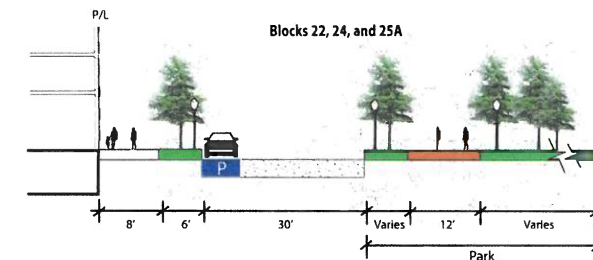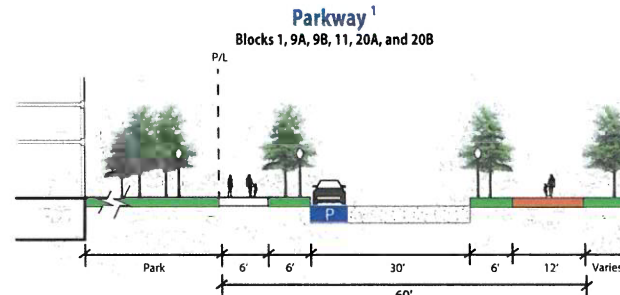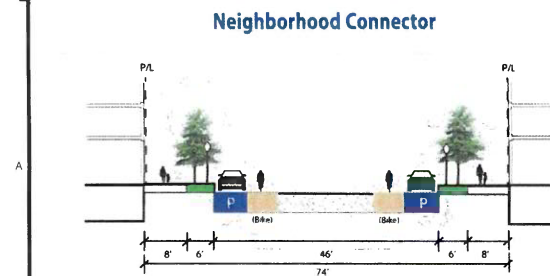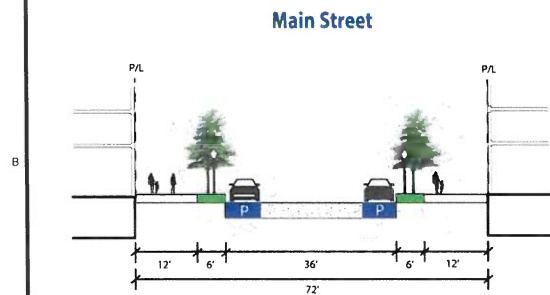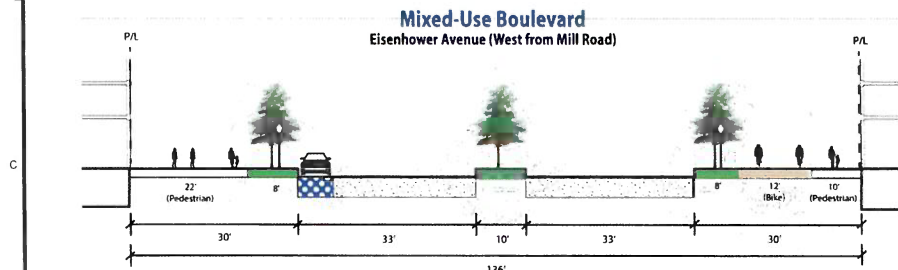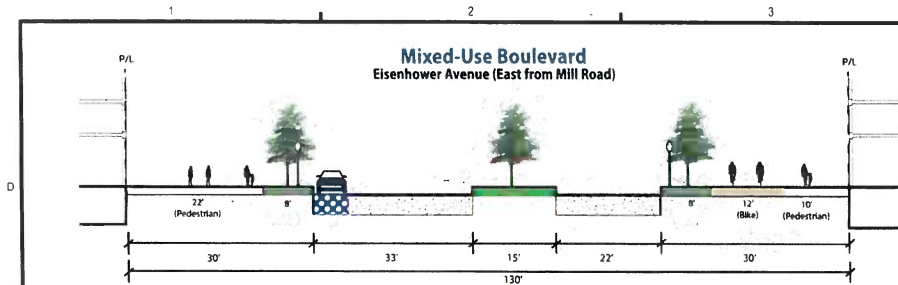

NOTE: THE STREET SECTIONS ADJACENT TO THE EISENHOWER METRO WILL BE MODIFIED VERSIONS OF THE NEIGHBORHOOD CONNECTOR AND PARKWAY STREET SECTIONS. THE STREET SECTIONS WILL NEED TO BE COORDINATED AND AGREED UPON WITH WMATA.

christopher consultants
4035 ridge top rd
alexandria, va 22304
engineering • surveying • land planning




COORDINATED DEVELOPMENT DISTRICT #2
CONCEPTUAL DESIGN PLAN
CITY OF ALEXANDRIA, VIRGINIA

NO.	DATE	DESCRIPTION
1	05/11/2022	CDD AMENDMENT SUBMISSION #1
2	07/01/2022	CDD AMENDMENT SUBMISSION #2
3	05/26/2023	CDD AMENDMENT SUBMISSION #3
4	11/02/2023	CDD AMENDMENT SUBMISSION #4

PROJECT No. 98085.060.00
DRAWING No. 111404
DATE 02/11/22
SCALE N/A
DESIGN EC
DRAWN HQ
CHECKED JMW

STREET CROSS SECTION EXHIBIT

SHEET No. **C600**

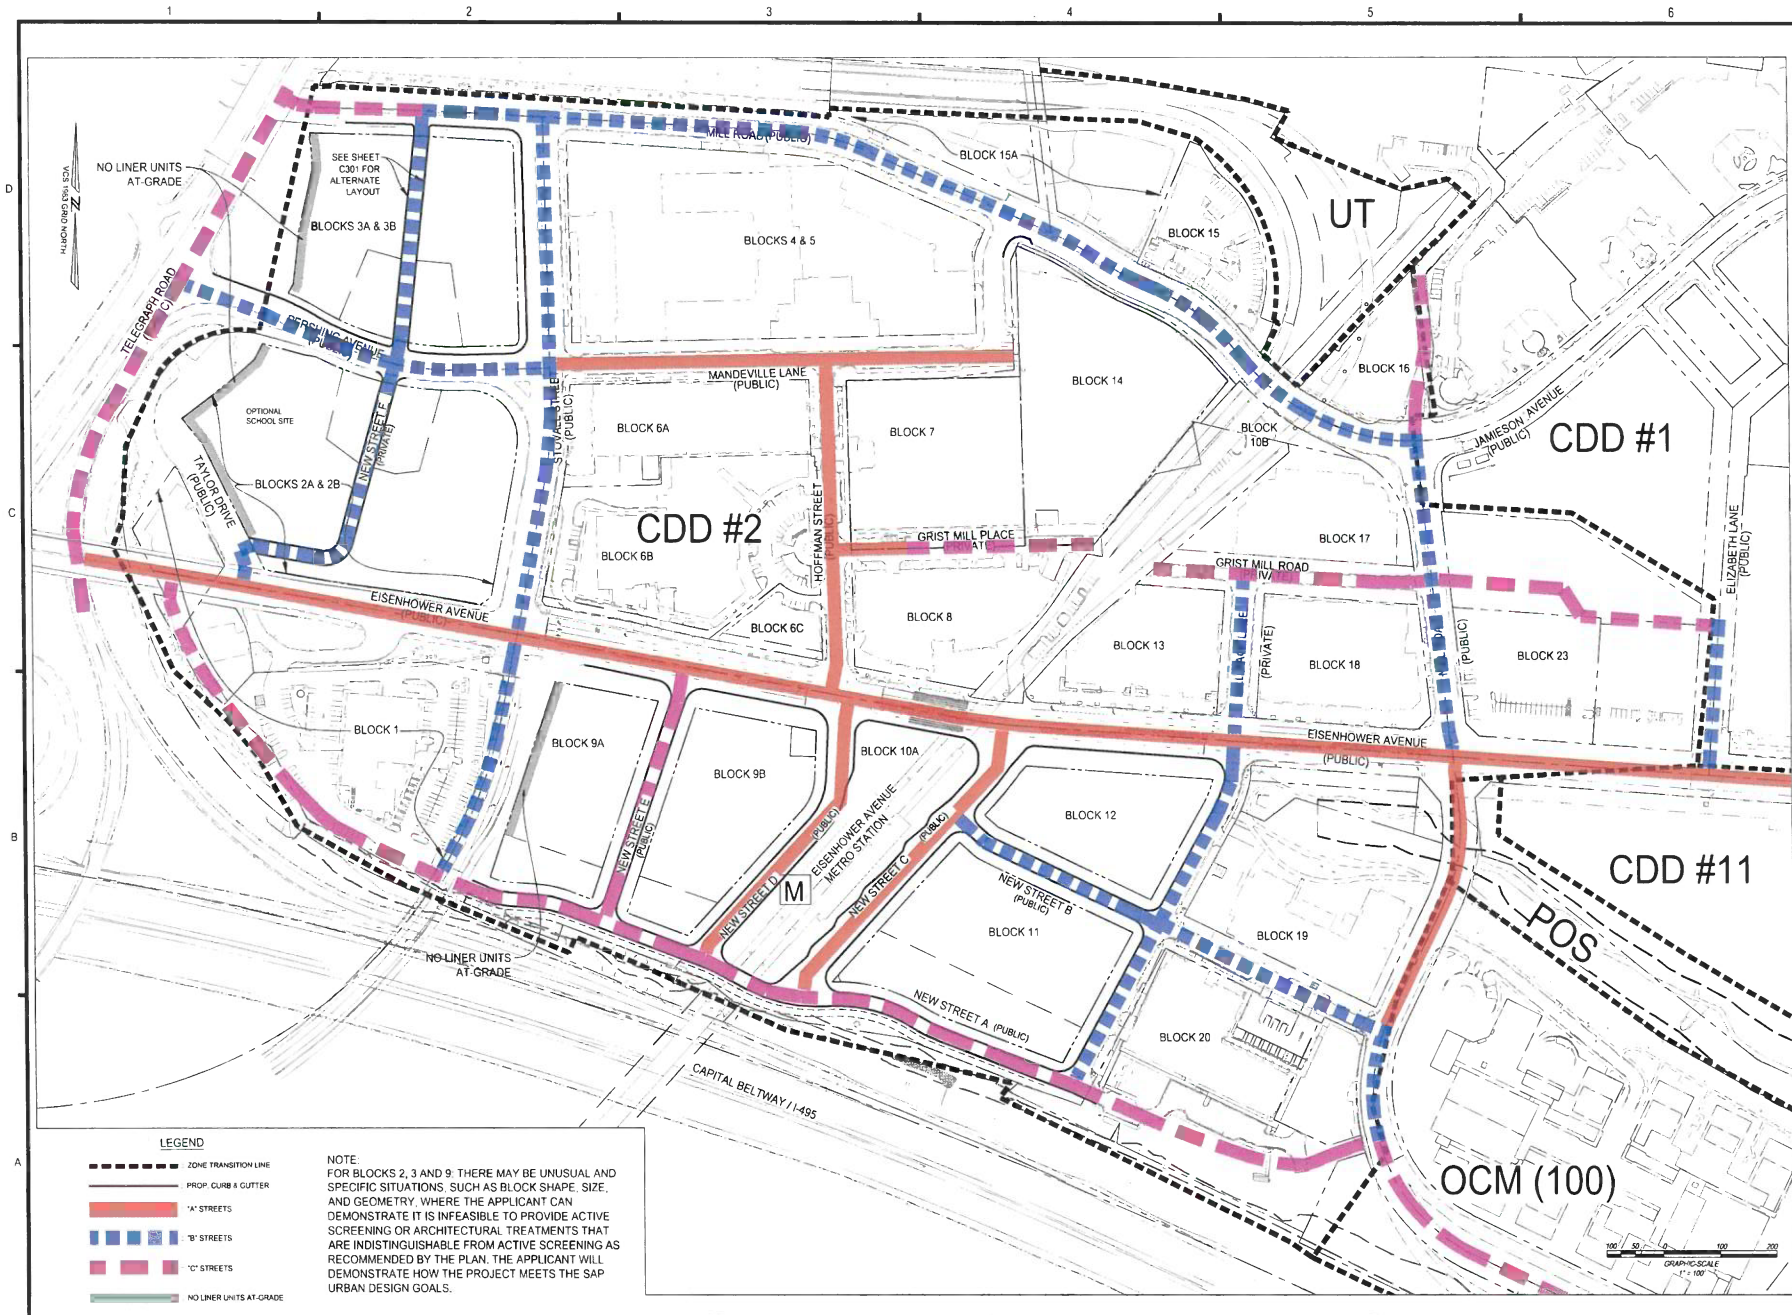

christopher consultants
4035 ridge top rd
suite 601
fairfax, va 22030
engineering • surveying • land planning




COORDINATED DEVELOPMENT DISTRICT #2
CONCEPTUAL DESIGN PLAN
CITY OF ALEXANDRIA, VIRGINIA

NO.	DATE	DESCRIPTION
1	05-11-2021	CDD AMENDMENT SUBMISSION #1
2	07-01-2022	CDD AMENDMENT SUBMISSION #2
3	05-19-2023	CDD AMENDMENT SUBMISSION #3
4	11-03-2023	CDD AMENDMENT SUBMISSION #4

PROJECT No. 98085.065.00
DRAWING No. 111404
DATE: 02-11-22
SCALE: SEE SHEET
DESIGN: EG
DRAWN: HL
CHECKED: KAW

STREET HIERARCHY EXHIBIT

SHEET No.
C700

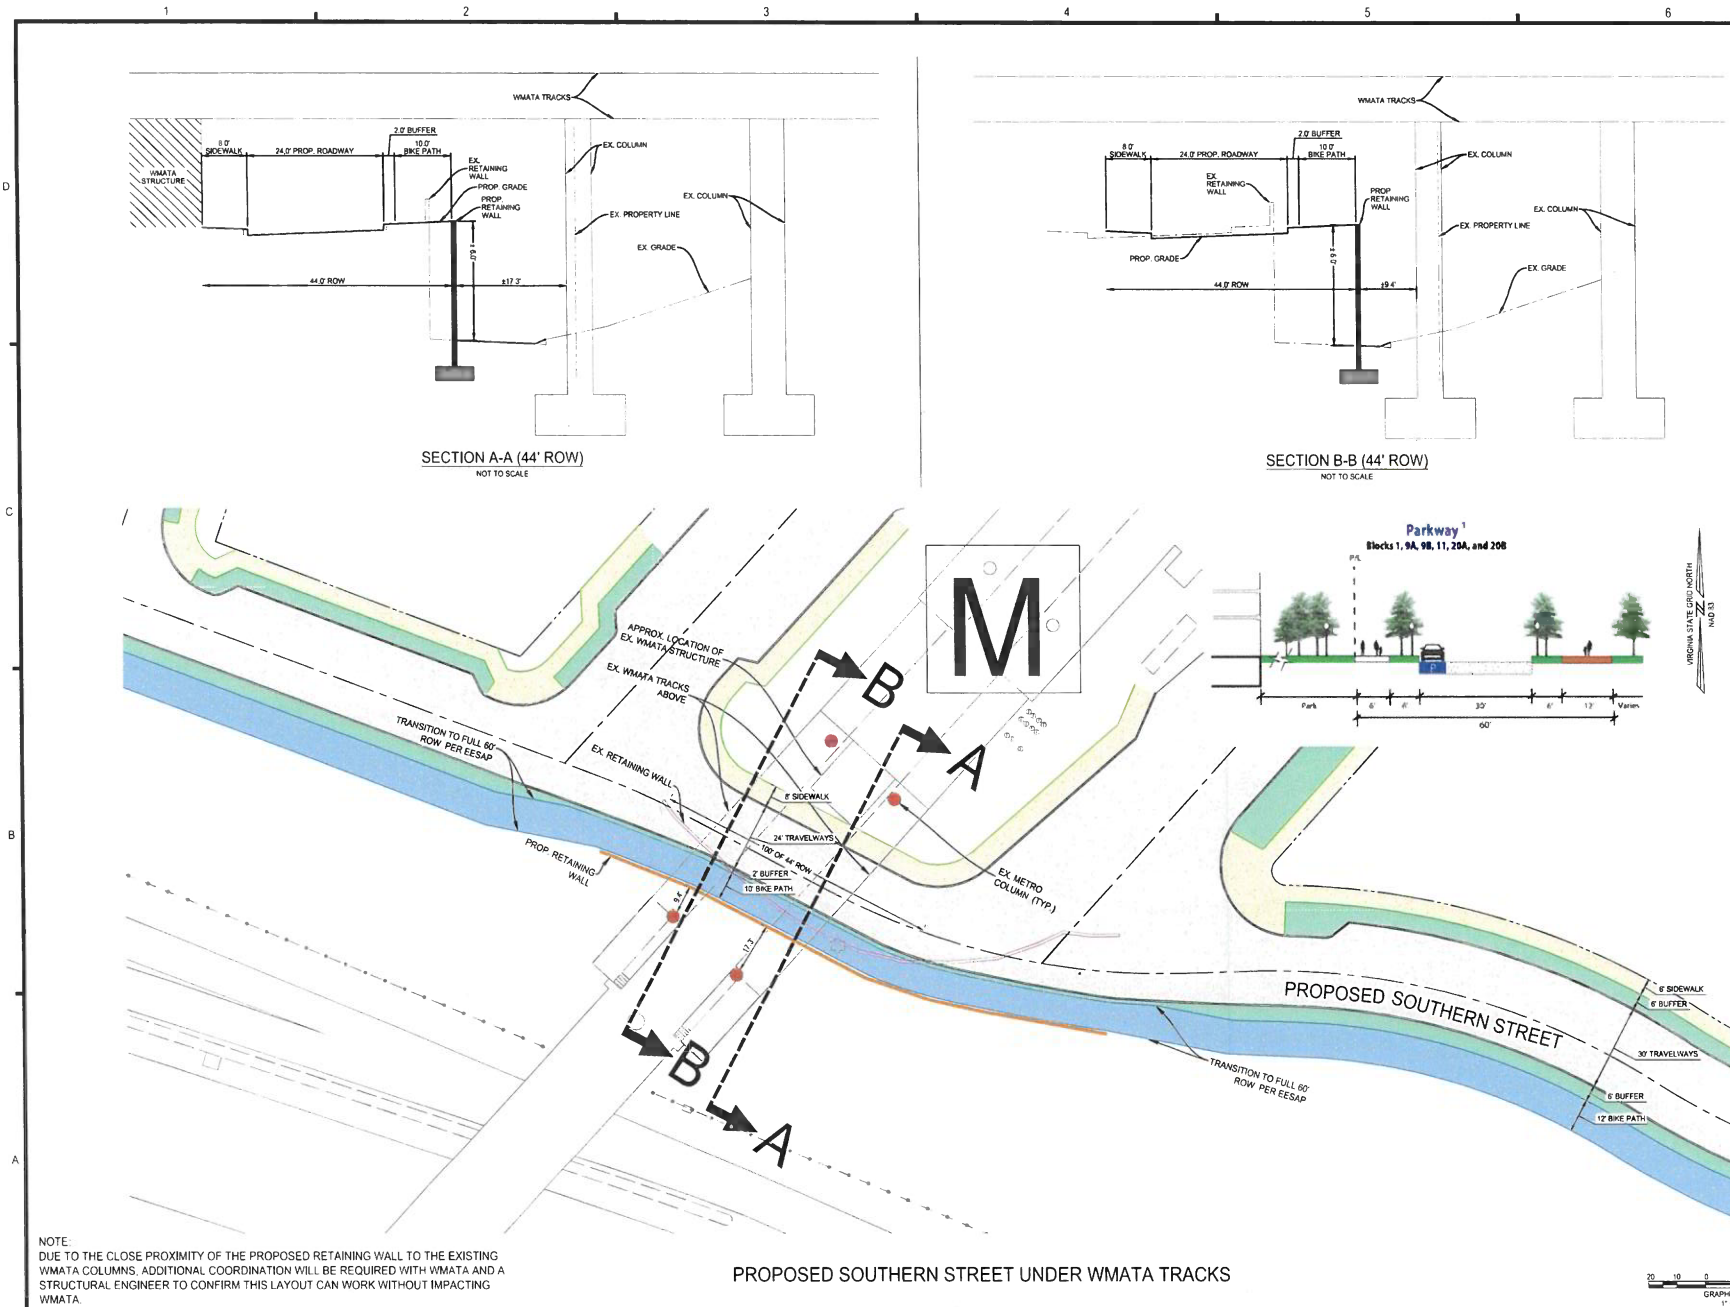

christopher consultants
4035 ridge top rd
alexandria, va 22304
p 703.273.8620
engineering • surveying • land planning



COORDINATED DEVELOPMENT DISTRICT #2
CONCEPTUAL DESIGN PLAN
CITY OF ALEXANDRIA, VIRGINIA

NO.	DATE	DESCRIPTION
1	08/11/2021	CDD AMENDMENT SUBMISSION #1
2	07/21/2022	CDD AMENDMENT SUBMISSION #2
3	05/16/2023	CDD AMENDMENT SUBMISSION #3
4	11/03/2023	CDD AMENDMENT SUBMISSION #4

PROJECT No. 98085.060.00
DRAWING No. 111404
DATE: 02/11/22
SCALE: SEE SHEET
DESIGN: EG
DRAWN: MO
CHECKED: JMW

SHEET TITLE
SOUTHERN STREET UNDER WMATA TRACKS EXHIBIT

SHEET NO.
C701